


CONCEPT, NOT FOR FABRICATION

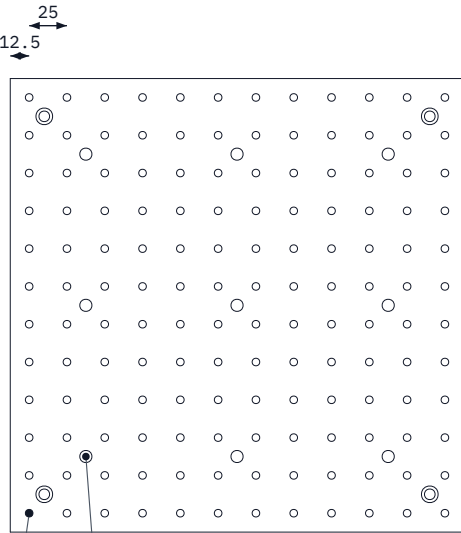


DETAIL A: TILE
Top view, scale 1:5

9 x 8 H7, 100 PITCH


144 x M6

DETAIL A NOTES


Holes continue the field grid
4 fixing holes, 7 mm, C'bore 11
Tile 12.7 thick on 5.3 packers

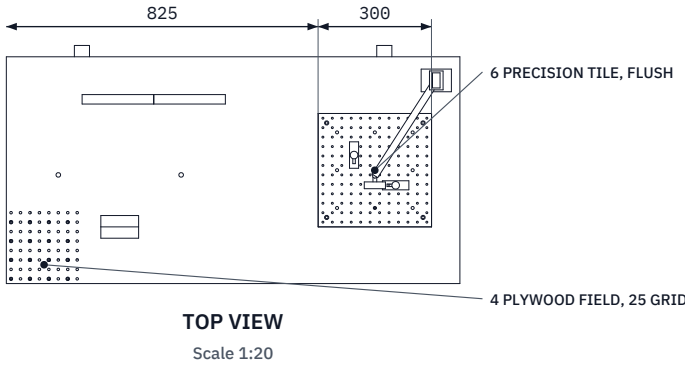


TOP VIEW
Scale 1:20

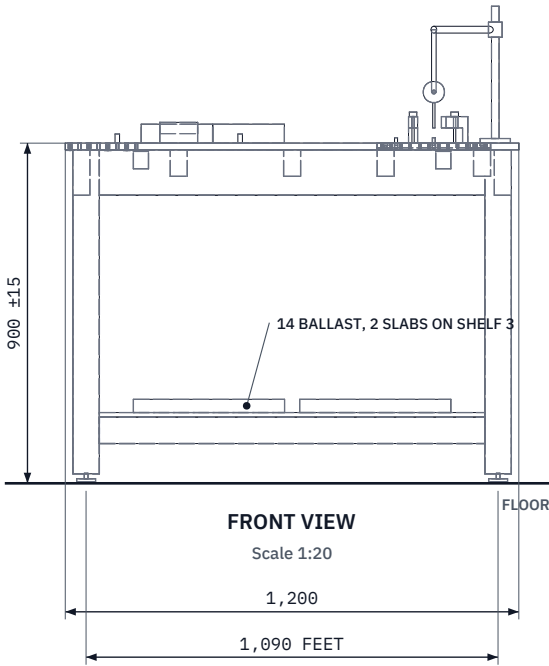

FRONT VIEW
Scale 1:20

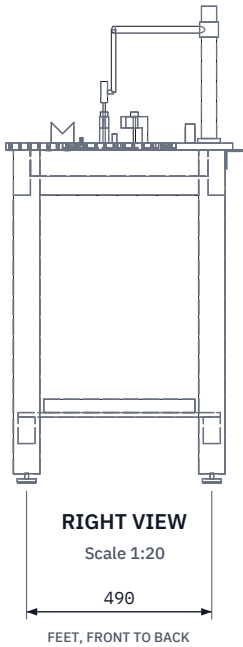

RIGHT VIEW
Scale 1:20

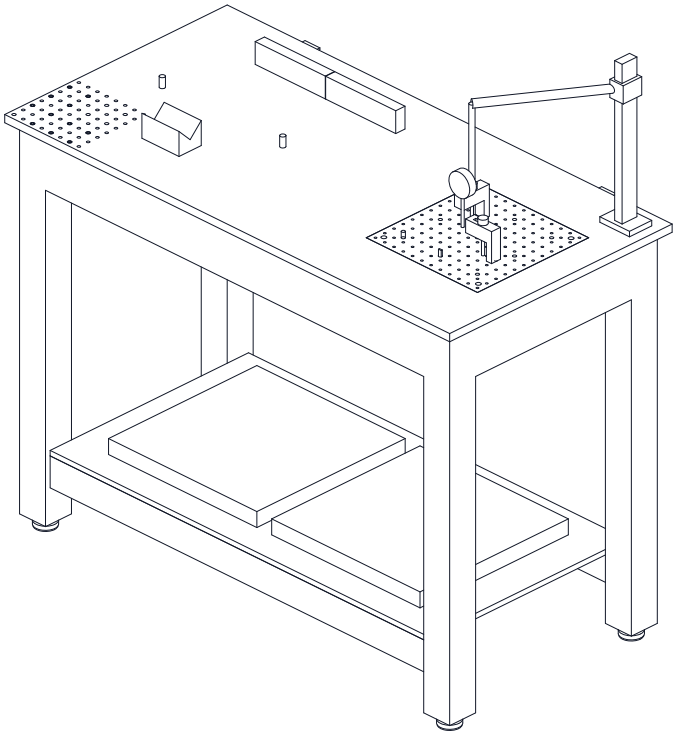

ISOMETRIC VIEW

Not to scale; worktop holes shown as a representative patch

MAIN DIMENSIONS AND INTERFACES (MM)

Worktop 1,200 x 600 x 18 birch ply, top at 900 ±15
Grid 25 pitch, first hole 12.5 from each edge; 1,152 positions
Field: 756 x 6.6 plain; 252 M6 on the 50 sub-grid; 130 tee nuts from below, 122 screw-in over frame
Tile 300 x 300 x 12.7, left edge 825 from the worktop's left edge
Feet at 1,090 x 490 centers; legs 70 square
Aprons 45 x 120; cross rails 45 x 70 at X -300, 0, 247.5, 502.5
Ballast 2 x 12.9 kg slabs (GBN-CAL-001, C4)
Toe clamp torque 1.6 N m max; one round + one diamond pin
Levelling feet with 3 mm rubber pads
All exposed edges chamfered or rounded 0.5 min
Third-angle; front view from -Y; origin at worktop center

GRIDBENCH

General arrangement

DRAWING NO. GBN-DWG-001			REV P2	SHEET 1 of 1	SIZE ANSI B
SCALE 1:20	UNITS mm	PROJECTION 	DATE 2026-09-25		DRAWN Amish Chadha
MATERIAL / NOTES Softwood frame, birch plywood top, cast aluminum tile; bought-in parts per bom/bom.csv. PRELIMINARY, NOT FOR FABRICATION					
Licensed CERN-OHL-S-2.0 · Design Molecule Lab · designmolecule.com				Generated from cad/src; do not edit by hand	